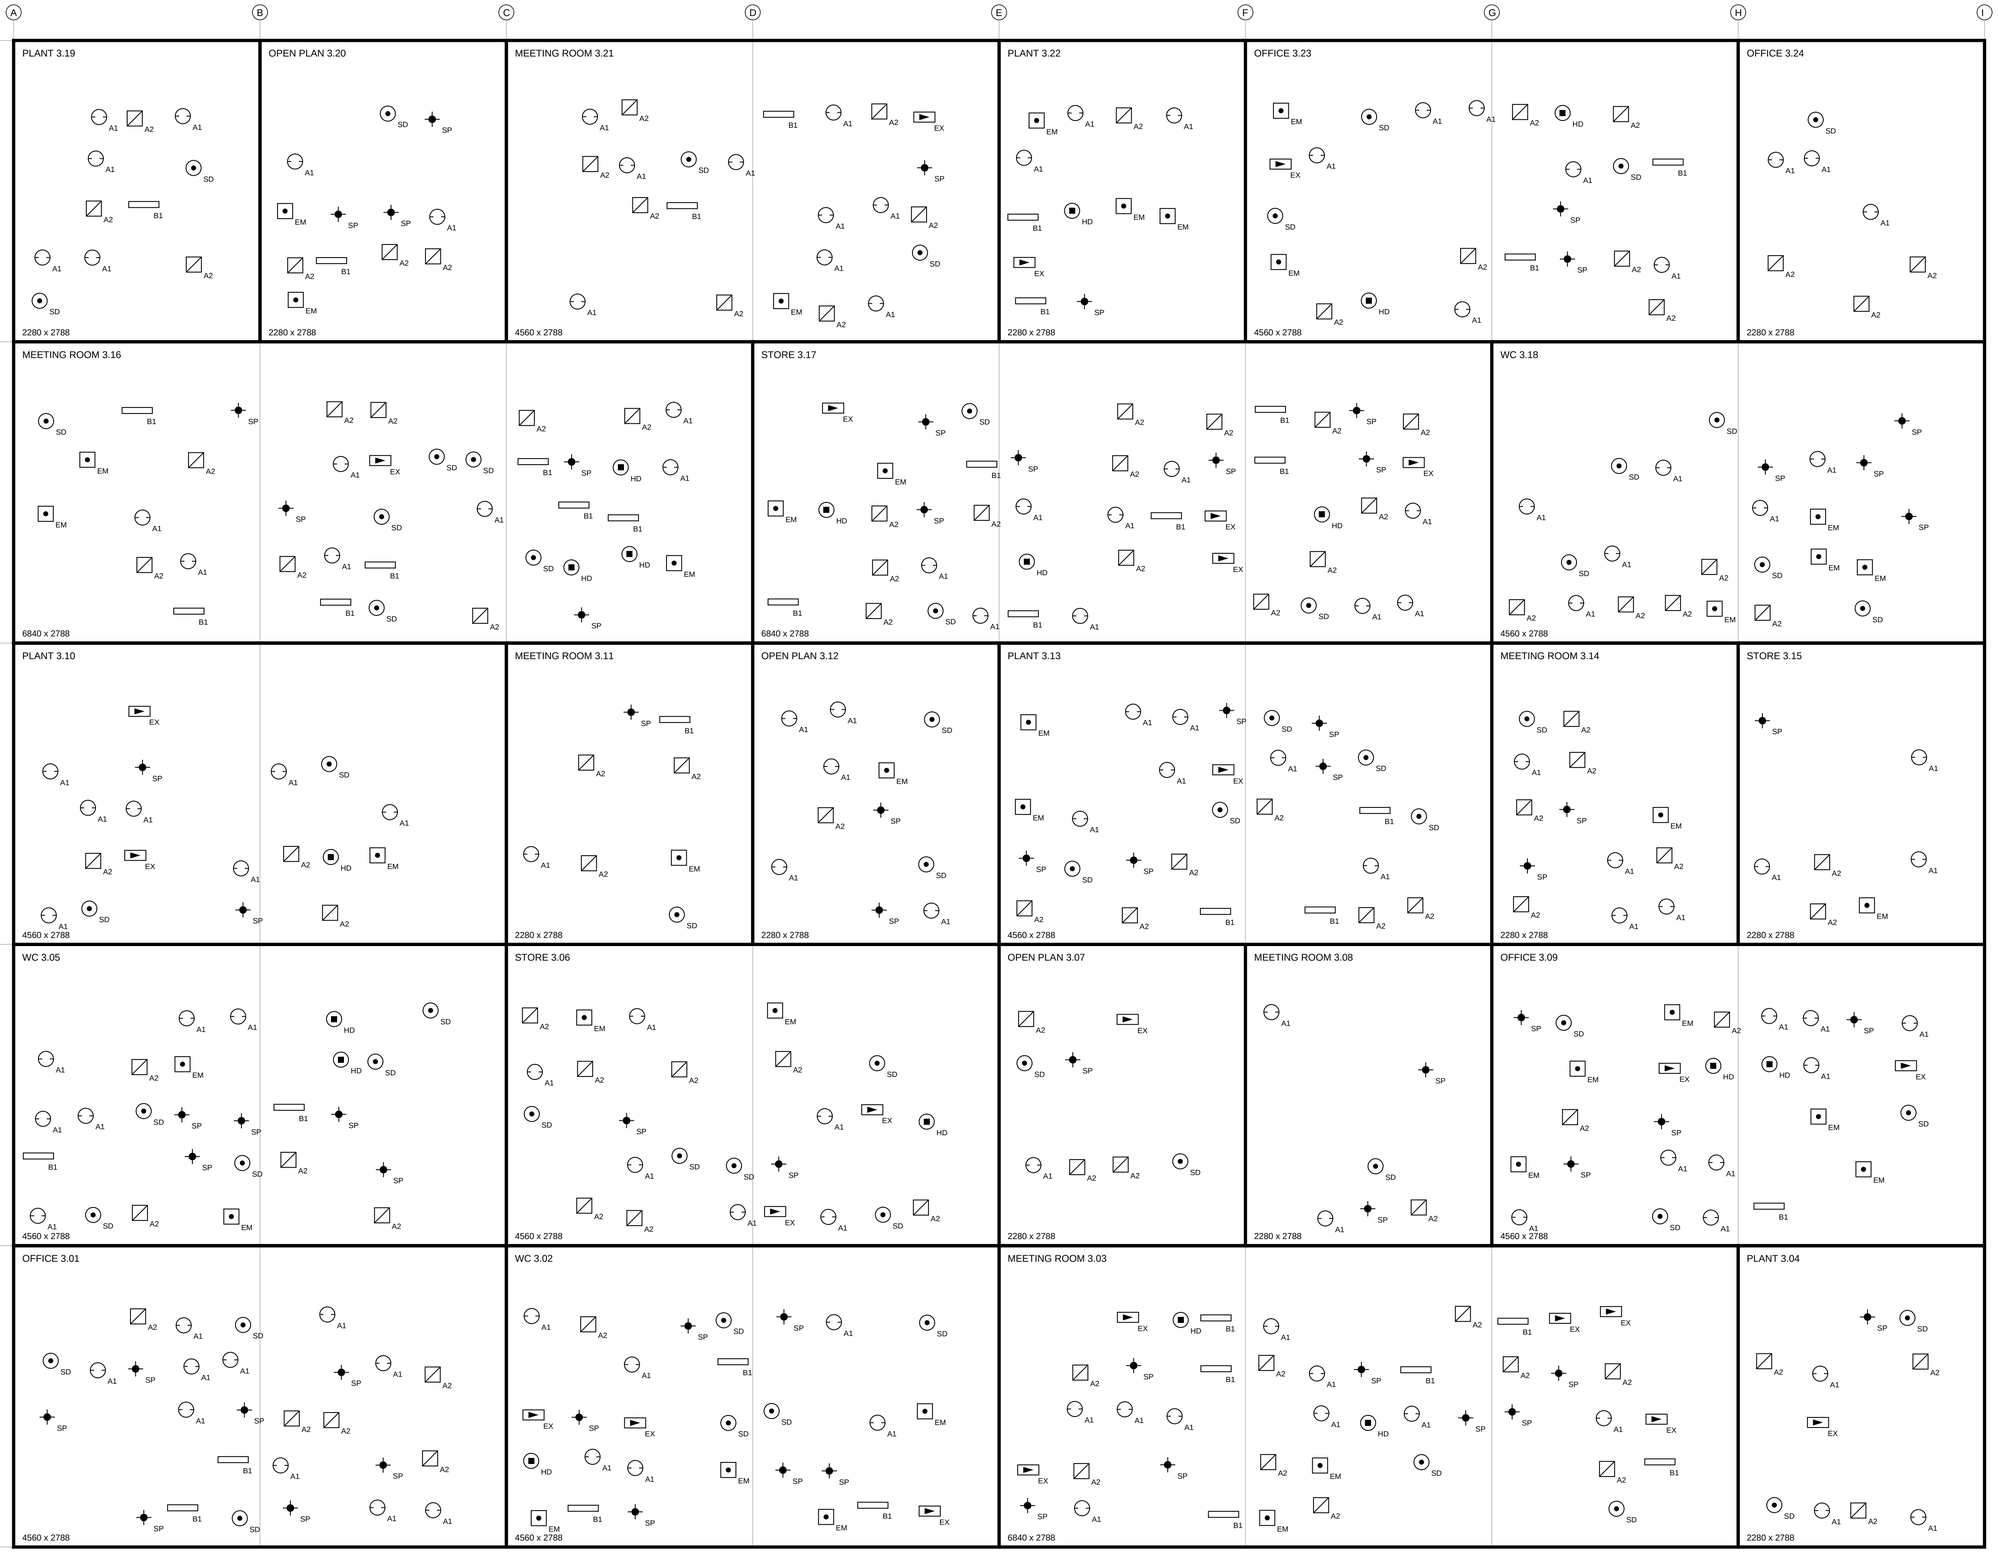

LEGEND

	A1	LED DOWNLIGHT, 150 MM, RECESSED
	A2	LED PANEL, 600 X 600 MM, RECESSED
	B1	LED LINEAR LUMINAIRE, 1200 MM, SURFACE MOUNTED
	EM	SELF-CONTAINED EMERGENCY LUMINAIRE, 3 HOUR
	EX	ILLUMINATED EXIT SIGN, MAINTAINED
	SD	OPTICAL SMOKE DETECTOR, CEILING MOUNTED, ADDRESSABLE
	HD	RATE-OF-RISE HEAT DETECTOR, CEILING MOUNTED, ADDRESSABLE
	SP	SPRINKLER HEAD, PENDENT, QUICK RESPONSE

NOTES

1. ALL TYPE A1 AND A2 LUMINAIRES TO BE DALI DIMMABLE.
2. SD AND HD DEVICES ARE ADDRESSABLE. REFER TO FIRE ALARM SCHEDULE.
3. SP HEADS AT 3.0 M CENTRES MAXIMUM, COORDINATE WITH CEILING GRID.
4. SSO MOUNTING HEIGHT 450 MM AFFL UNLESS NOTED OTHERWISE.

PROJECT	SYNTHETIC OFFICE FIT-OUT, BUILDING 7
DRAWING TITLE	LEVEL 3 LIGHTING AND FIRE ALARM LAYOUT
DRAWING NO	E-301
SCALE	1:100 @ A1
REV	P2
STATUS	TENDER

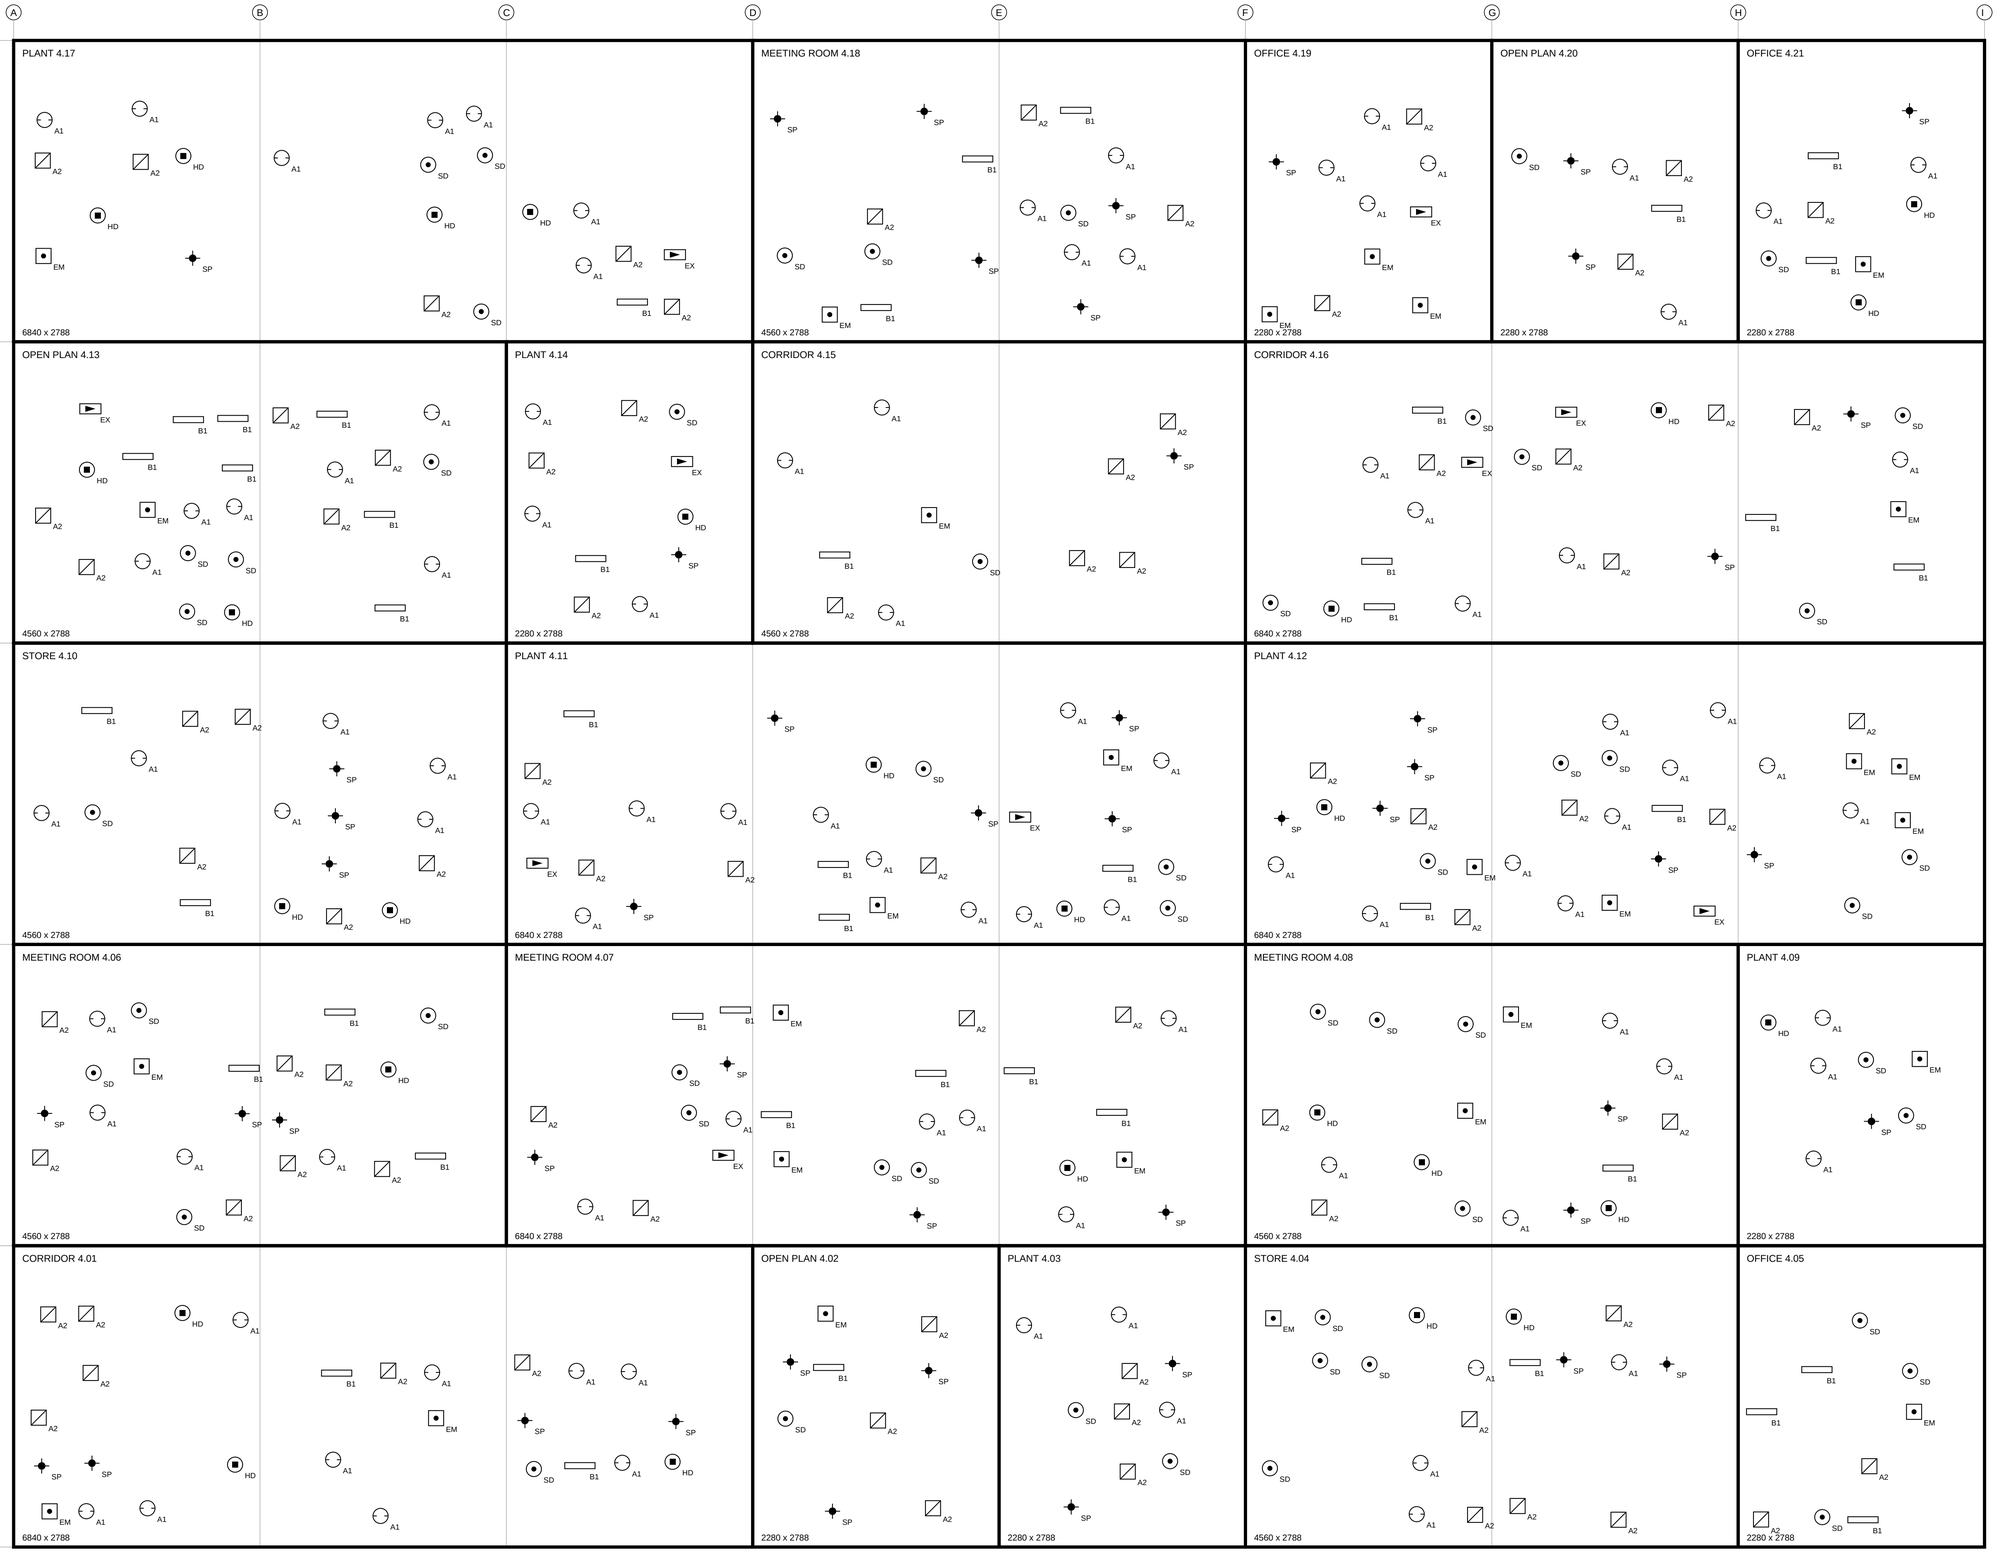

LEGEND

	A1	LED DOWNLIGHT, 150 MM, RECESSED
	A2	LED PANEL, 600 X 600 MM, RECESSED
	B1	LED LINEAR LUMINAIRE, 1200 MM, SURFACE MOUNTED
	EM	SELF-CONTAINED EMERGENCY LUMINAIRE, 3 HOUR
	EX	ILLUMINATED EXIT SIGN, MAINTAINED
	SD	OPTICAL SMOKE DETECTOR, CEILING MOUNTED, ADDRESSABLE
	HD	RATE-OF-RISE HEAT DETECTOR, CEILING MOUNTED, ADDRESSABLE
	SP	SPRINKLER HEAD, PENDENT, QUICK RESPONSE

NOTES

1. ALL TYPE A1 AND A2 LUMINAIRES TO BE DALI DIMMABLE.
2. SD AND HD DEVICES ARE ADDRESSABLE. REFER TO FIRE ALARM SCHEDULE.
3. SP HEADS AT 3.0 M CENTRES MAXIMUM, COORDINATE WITH CEILING GRID.
4. SSO MOUNTING HEIGHT 450 MM AFFL UNLESS NOTED OTHERWISE.

PROJECT	SYNTHETIC OFFICE FIT-OUT, BUILDING 7
DRAWING TITLE	LEVEL 4 LIGHTING AND FIRE ALARM LAYOUT
DRAWING NO	E-302
SCALE	1:100 @ A1
REV	P2
STATUS	TENDER